

電梯額定速度	A 減速距離
15M /min	400mm
30M /min	800mm
45M /min	1100mm
60M /min	1500mm
	B 減速距離
90M /min	2100mm
105M/min	2400mm
120M/min	2800mm
150M/min	2100mm
150M/Min減速距離=Address A5-05,04 (A1500+B2100)=3600mm	

注意


HOU上緣 及 HOD下緣必須與水平遮板總長度切齊

HOU , HOD , 可為 A 或 B 接點開關 由ADDRESS A2-01, Bit 0 設定, 內定為 A 接點開關

DZ 必須為 A 接點開關, 為到樓提前開門及開門鋼索伸長補正用, 無此功能電梯不用裝設(A2=02, Bit1=1)

US, DS, HUS, HDS 可為 A 或 B 接點開關 由ADDRESS A2-01, Bit 1 設定, 內定為 B 接點開關

Adress A2-01, Bit7=1時,
US/DL=手動終點(無機房電梯時, 手動終點安全距離應在1800mm以上)

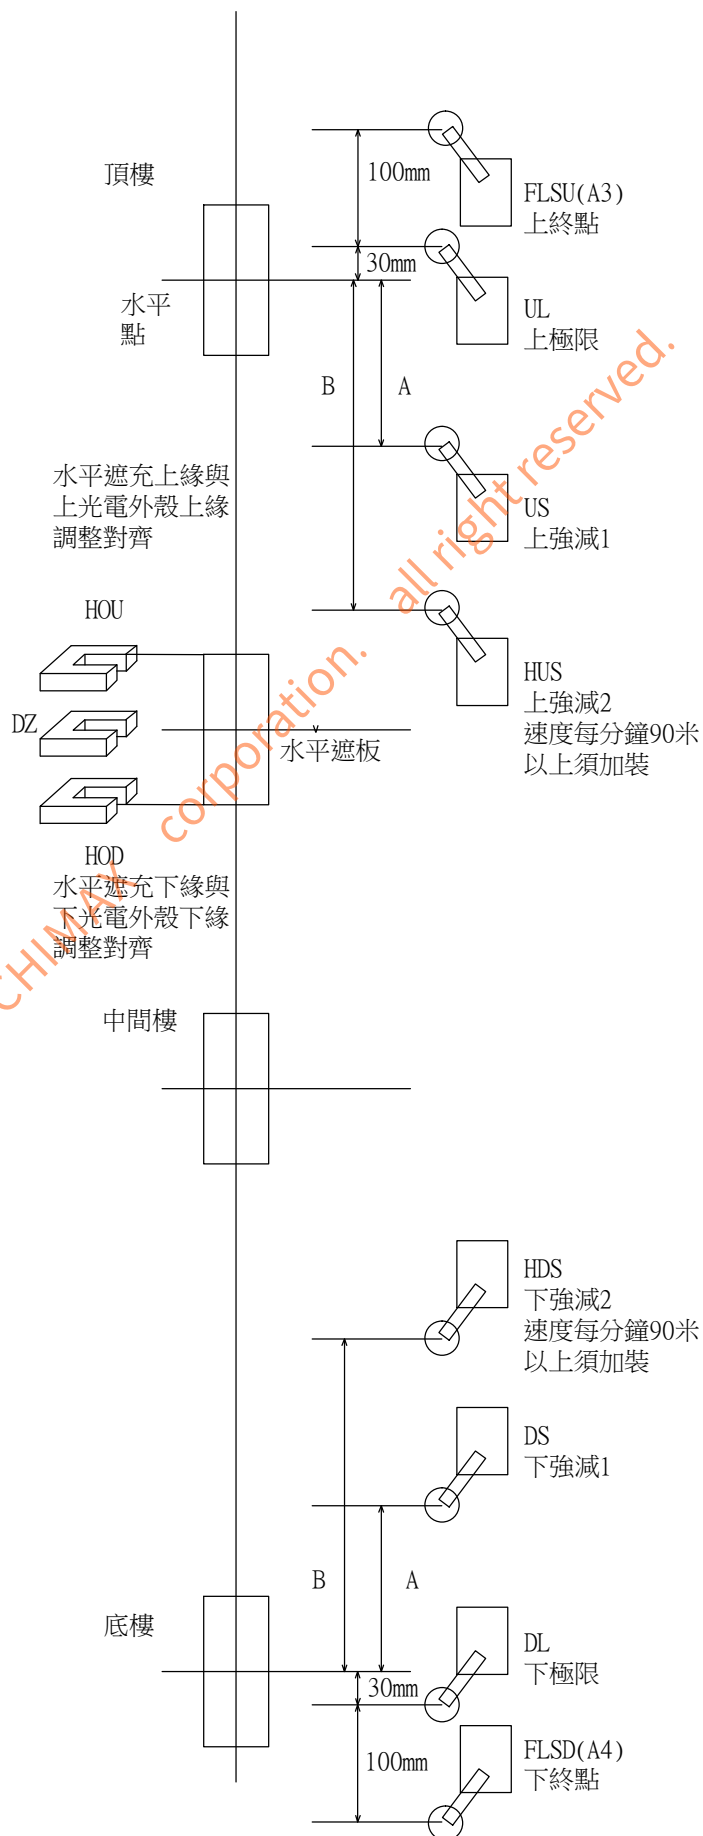

修訂	111.02.01配合藍綠版修訂		
圖名	圖面說明		
圖號	定位回路	日期	
	繪圖	LIANG	