

UCDH叫車及顯示基板：

1. 可用於乘場外叫車及樓層，狀態顯示

傳輸站號 = 0~32, 不可重複設置

站號0 = 顯示

站號1~32 = 乘場外叫 (附行動不便叫車)

用於外叫車時2.5/3PIN 插座狀態

1=UP 2=DN 3=PUP 4=PDN 5=LUP 6=LDN


2. 可用於車廂七個樓層內之叫車及樓層，狀態顯示

站號33~36 = 一般車廂叫車

站號37~40 = 行動不便車廂叫車


用於內叫車時2.5/3PIN 插座狀態

1=1F 2=2F 3=3F 4=4F 5=5F 6=6F 7=7F 8=8F

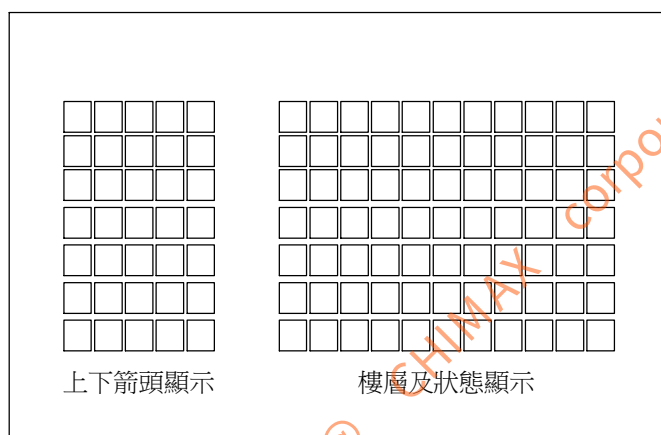

點陣顯示

1. 保養
2. 停用
3. 停電
4. 消防
5. 管制
6. 超載
7. 滿載
8. 使用

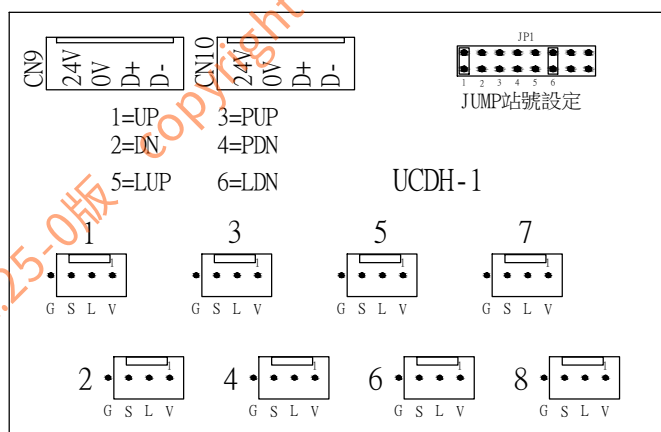

基板尺寸：長63*寬105mm

基板孔距：長57*寬99mm(Φ3.3)

點陣視窗：長40*寬91mm

元件高度：含插頭接線33mm

修訂	111.02.01配合藍錄版修訂		
圖面說明			
圖名	UCDH	日期	
圖號		繪圖	LIANG