

傳輸站號設定 (位址)


乘場 01~08 (A1-00) 乘場 09~16 (A1-01)

乘場 17~24 (A1-02) 乘場 25~32 (A1-03)

有使用站號相對應位址內對應站號位元需設定為 "1"

EX: 1F~11F (位址A1-00=1111 1111=FF H)

(位址A1-01=0000 0111=07 H)

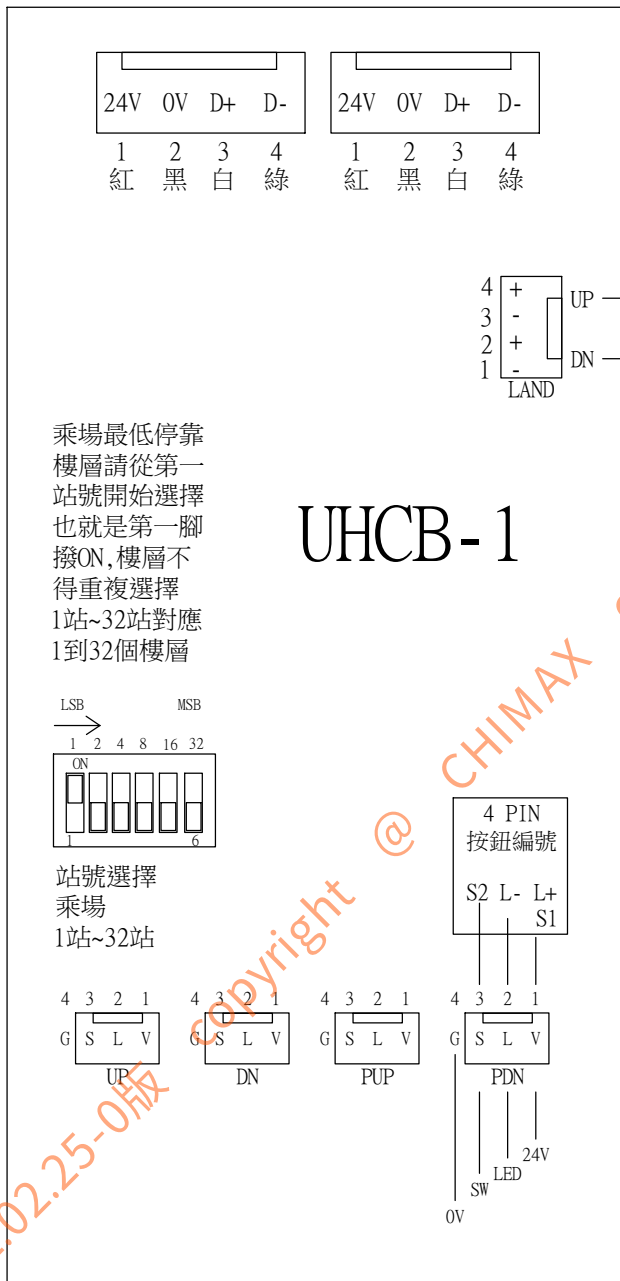

基板尺寸: 長120*寬65mm

點陣視窗: 長64.3*寬64.3mm

固定孔距: 長113.5*寬58.5mm (Φ3.3mm)

元件高度: 連插頭線組高度33mm

修訂	111.02.01配合藍錄版修訂		
圖面說明			
圖名	UHCB外叫板	日期	
圖號		繪圖	LIANG